Общество с ограниченной ответственностью «Проектная компания «КиТ»
197371, город Санкт-Петербург, Комендантский проспект, дом 53 корпус 3,
литера А, помещение 7-н офис 101;
ИНН 7813600590; КПП 781401001;
р/с 40702810432280000873 в филиале «Санкт-Петербургский»
ОАО «АЛЬФА-БАНК» к/с 30101810600000000786
БИК 044030786 ОКПО 92072639;
ОКВЭД 74.20.11, 74.20.12, 74.20.13, 74.20.3, 74.20.4
Регистрационный номер члена в реестре СРО: П-019-7813600590
http://www.pkkit.ru, e-mail: mail@pkkit.ru
тел./факс +7 (812) 925-54-01

Экз. № ___

«Здание магазина» по адресу:
Ленинградская область, Сланцевский район, г. Сланцы, ул. Маяковского, д. 18
кадастровый номер земельного участка - 47:28:0301052:16

ПРОЕКТНАЯ ДОКУМЕНТАЦИЯ

Раздел 3
Объемно-планировочные и архитектурные решения

Объемно-планировочные и архитектурные решения

Шифр: 06-06/24-АР

г. Санкт-Петербург
2024 г.

Генеральный директор
ООО «ПК «КиТ»

_____ Тузов Д.Е.

«Здание магазина» по адресу:

Ленинградская область, Сланцевский район, г. Сланцы, ул. Маяковского, д. 18

кадастровый номер земельного участка - 47:28:0301052:16

ПРОЕКТНАЯ ДОКУМЕНТАЦИЯ

Раздел 3
Объемно-планировочные и архитектурные решения

Объемно-планировочные и архитектурные решения

Шифр: 06-06/24-АР

Главный инженер проекта Г.В. Гущин

г. Санкт-Петербург
2024 г.

Содержание Тома

Лист		Наименование	Примечание
1	06-06/24-АР-С	Содержание тома	
		Текстовая часть	
1	06-06/24-АР-ТЧ	Общие данные	
1	06-06/24-АР-ТЧ	а). описание и обоснование внешнего и внутреннего вида объекта капитального строительства, его пространственной, планировочной и функциональной организации	
2	06-06/24-АР-ТЧ	б) обоснование принятых объемно-пространственных и архитектурно-художественных решений, в том числе в части соблюдения предельных параметров разрешенного строительства объекта капитального строительства	

Согласовано

Взам. инв. №

Подп. И дата

Инв. № подл.

Изм	Кол.уч	Лист	Лист	Подпись	Дата	06-06/24-АР-С		
Разраб.		Кораблев			08.24	Содержание тома	Стадия	Лист	Листов
Проверил		Гущин			08.24		П	1	3
							ООО «ПК «КиТ»		
Н.контрол		Лебедев			08.24				
ГИП		Гущин			08.24				

Копировал

Ф

2	06-06/24-АР-ТЧ	б(1) обоснование принятых архитектурных решений в части обеспечения соответствия зданий, строений и сооружений установленным требованиям энергетической эффективности (за исключением зданий, строений, сооружений, на которые требования энергетической эффективности не распространяются)	
3	06-06/24-АР-ТЧ	б(2) перечень мероприятий по обеспечению соблюдения установленных требований энергетической эффективности к архитектурным решениям, влияющим на энергетическую эффективность зданий, строений и сооружений (за исключением зданий, строений, сооружений, на которые требования энергетической эффективности не распространяются)	
4	06-06/24-АР-ТЧ	б(3) описание и обоснование принятых архитектурных решений, направленных на повышение энергетической эффективности объекта капитального строительства;	
4	06-06/24-АР-ТЧ	в) описание и обоснование использованных композиционных приемов при оформлении фасадов и интерьеров объекта капитального строительства;	

4	06-06/24-АР-ТЧ	г) описание и обоснование решений по отделке помещений основного, вспомогательного, обслуживающего и технического назначения;	
4	06-06/24-АР-ТЧ	д) описание архитектурных решений, обеспечивающих естественное освещение помещений с постоянным пребыванием людей;	
4	06-06/24-АР-ТЧ	д(1) результаты расчетов продолжительности инсоляции и коэффициента естественной освещенности;	
5	06-06/24-АР-ТЧ	е) описание архитектурно-строительных мероприятий, обеспечивающих защиту помещений от шума, вибрации и другого воздействия;	
5	06-06/24-АР-ТЧ	ж) описание решений по светоограждению объекта, обеспечивающих безопасность полета воздушных судов (при необходимости);	
5	06-06/24-АР-ТЧ	з) описание и обоснование принятых объемно-планировочных решений объекта капитального строительства, обеспечивающих в том числе соблюдение санитарно-эпидемиологических требований;	
6	06-06/24-АР-ТЧ	з(1) сведения о номенклатуре, компоновке и площадях основных производственных, экспериментальных, сборочных, ремонтных	

		и иных цехов, а также лабораторий, ангарских и административно-бытовых помещений, иных помещений вспомогательного и обслуживающего назначения – для объектов производственного назначения;	
6	06-06/24-АР-ТЧ	з(2) обоснование номенклатуры, компоновки и площадей помещений основного, вспомогательного, обслуживающего назначения и технического назначения – для объектов непроизводственного назначения;	
		Графическая часть	
1	06-06/24-АР, лист 1	План на отм. ±0.000. Разрез 1-1 М 1:100	
2	06-06/24-АР, лист 2	Фасады 1-8, 8-1, А-Г, Г-А М 1:100	

а) описание внешнего вида объекта капитального строительства, описание и обоснование пространственной, планировочной и функциональной организации объекта капитального строительства;

Объемно-планировочные решения здания приняты исходя из особенностей его функционально-технологического предназначения, допустимых размеров застройки и рельефа площадки.

Принятое планировочной решение продиктовано конфигурацией участка и ориентацией лицевого фасада здания. Проектом предлагается входную группу расположить с западной стороны здания.

Проектируемое здание магазина представляет собой одноэтажное здание прямоугольной формы. Размеры здания – 18,50 * 30,50 м. Высота здания от земли – 5,20 м.

Проектируемое здание – металлическое каркасно-связевое, с ограждающими конструкциями из сэндвич-панелей, окнами из ПВХ профиля с однокамерными стеклопакетами.

В здании предполагается размещение магазина (пункта) выдачи товаров магазина дистанционной торговли.

Проектом предусмотрена свободная планировка.

Планировка помещений выполняется после ввода объекта в эксплуатацию арендаторами самостоятельно с соблюдением действующих нормативных требований.

В магазине предполагается размещение объекта торгового назначения: супермаркет, осуществляющий продажу продовольственных и непродовольственных товаров повседневного спроса.

На 1-м этаже размещены:

- Торговая зона, зона хранения товаров и подсобные помещения.

Класс функциональной пожарной опасности Ф 3.1.

Степень огнестойкости IV.

Класс конструктивной пожарной опасности С0.

б) обоснование принятых объемно-пространственных и архитектурно-художественных решений, в том числе в части соблюдения предельных параметров разрешенного строительства, реконструкции объекта капитального строительства;

В соответствии с ПЗЗ Сланцевского городского поселения Сланцевского муниципального района Ленинградской области участок проектирования расположен в территориальной зоне О-2 «Зона делового общественного и коммерческого назначения».

При проектировании объекта учтены все предельные параметры разрешенного строительства объекта в соответствии с правилами землепользования и застройки:

- площадь застройки объекта не превышает разрешенный ПЗЗ максимальный процент застройки в границах земельного участка – 70%. Площадь застройки объекта составляет 573,5 кв.м. (7,67 % от площади земельного участка). Требование соблюдается.

- предельное количество этажей – 8 этажей, предельная высота зданий – 32 м. Запроектировано одноэтажное здание высотой 5,2 м.

Принятые объемно-пространственное и архитектурно-художественное решение продиктованы местоположением и назначением объекта.

Назначение объекта соответствует основному виду разрешенного использования – «Магазины».

При проектировании объекта учтены противопожарные мероприятия, в том числе:

В целях соблюдения норм пожарной безопасности к строительству применены материалы, отвечающие требованиям к IV степени огнестойкости.

Для защиты людей и имущества от опасных факторов пожара и ограничения его воздействий создания системы противопожарной защиты в проекте предусматриваются следующие мероприятия:

- соблюдена допустимая площадь здания определенного класса функциональной пожарной опасности, площади пожарного отсека в зависимости от степени огнестойкости здания и класса конструктивной пожарной опасности и класса функциональной пожарной опасности в соответствии с СП 2.13130.2020;

- принятые объёмно-пространственные решения, обеспечивающие ограничение распространения пожара за пределы очага;

– предусмотрено устройство необходимого количества и размеров эвакуационных выходов для обеспечения безопасной эвакуации людей;

– здание обеспечено путями эвакуации, удовлетворяющими требованиям безопасной эвакуации при пожаре;

– обеспечены условия для деятельности пожарных подразделений по проведению спасательных работ и тушению пожара, доставки средств пожаротушения в любое помещение здания;

– строительные конструкции здания выполнены с пределами огнестойкости и классами пожарной опасности, соответствующими требуемым показателям пожарной опасности здания;

– на путях эвакуации применены отделочные материалы, ограничивающие пожарную опасность поверхностных слоёв.

Детально мероприятия по обеспечению пожарной безопасности описываются в разделе Раздел 9 проектной документации «Мероприятия по обеспечению пожарной безопасности».

б(1) обоснование принятых архитектурных решений в части обеспечения соответствия зданий, строений и сооружений установленным требованиям энергетической эффективности (за исключением зданий, строений, сооружений, на которые требования энергетической эффективности не распространяются);

Для обеспечения соответствия проектируемого здания требованиям энергетической эффективности приняты архитектурные решения минимизирующие телопотери и затраты энергетических ресурсов.

Комплекс взаимосвязанных энергосберегающих мероприятий:

– выбор оптимальной формы здания, характеризующейся пониженным коэффициентом компактности и обеспечивающей минимальные теплопотери в зимний период и минимальные теплопоступления в летний период года;

– сокращение площади наружных ограждающих конструкций путем уменьшения периметра наружных стен за счет отказа от изрезанности фасадов, выступов, западаний и т.п.;

– использование естественного освещения помещений для снижения затрат электрической энергии;

– связь помещений без излишних коридоров, холлов.

Выбор архитектурных решений, принятых в части обеспечения энергоэффективности здания, является оптимальным. Он позволяет исключить

нерациональный расход энергоресурсов и отвечает требованиям, изложенным в СП 50.13330.2012 «Тепловая защита зданий» Актуализированная редакция СНиП 23-02-2003:

- тепловой защиты здания;
- энергоэффективность расхода энергии на отопление и вентиляцию;
- обеспечение заданных параметров микроклимата помещений за счет ограждающих конструкций;
- надежность и долговечность.

Теплозащитная оболочка здания отвечает следующим условиям:

а) приведенное сопротивление теплопередаче отдельных ограждающих конструкций не меньше нормируемых значений;

б) удельная теплозащитная характеристика здания не больше нормируемого значения;

в) температура на внутренних поверхностях ограждающих конструкций не ниже минимально допустимых значений (санитарно-гигиеническое требование).

б(2) перечень мероприятий по обеспечению соблюдения установленных требований энергетической эффективности к архитектурным решениям, влияющим на энергетическую эффективность зданий, строений и сооружений (за исключением зданий, строений, сооружений, на которые требования энергетической эффективности не распространяются);

К мероприятиям по обеспечению установленных требований к энергоэффективности здания относятся:

- утепление наружных стен и покрытия здания;
- непрерывный контур утепления;
- применением эффективного утеплителя в составе ограждающих конструкций.
- устройство входных групп с применением утепленных наружных дверей с коэффициентом приведенного сопротивления теплопередаче в соответствии с теплотехническим расчетом;
- установка доводчиков входных дверей;
- применение дверных и оконных блоков (витражей) из ПВХ с коэффициентом приведенного сопротивления теплопередаче в соответствии с теплотехническим расчетом.

б(3) описание и обоснование принятых архитектурных решений, направленных на повышение энергетической эффективности объекта капитального строительства;

Для отделки фасадов применяются материалы, согласно заданию Заказчика. Здание выполняется из связевого металлического каркаса с ограждающими конструкциями из сэндвич-панелей.

Входные двери выполнены из ПВХ (металлопластика) профиля с однокамерными стеклопакетами.

Оконные переплеты из ПВХ профиля.

в) описание и обоснование использованных композиционных приемов при оформлении фасадов и интерьеров объекта капитального строительства;

Для отделки фасадов применяются материалы, согласно заданию Заказчика. Здания выполняются из сэндвич-панелей, которые несут ограждающую и в то же время эстетическую функции, так как не требуют дополнительной отделки.

Здание имеет прямоугольную форму в плане. В композиционном решении присутствуют элементы симметрии вдоль главной линии фасада создаваемые порядком симметрично расположенных окон и дверей относительно центрального входа в здание.

Интерьеры выполняется арендаторами после ввода объекта в эксплуатацию.

г) описание и обоснование решений по отделке помещений основного, вспомогательного, обслуживающего и технического назначения;

Отделка помещений основного, вспомогательного, обслуживающего и технического назначения выполняется арендаторами после ввода объекта в эксплуатацию.

д) описание архитектурных решений, обеспечивающих естественное освещение помещений с постоянным пребыванием людей;

Естественное освещение предусмотрено через оконные проёмы на фасадах.

Помещения с постоянным пребыванием людей на объекте отсутствуют.

д(1) результаты расчетов продолжительности инсоляции и коэффициента естественной освещенности;

Нормируемые помещения с постоянным пребыванием людей на объекте отсутствуют.

е) описание архитектурно-строительных мероприятий, обеспечивающих защиту помещений от шума, вибрации и другого воздействия;

Для защиты от воздействия наружного шума и вибрации, приняты следующие строительные и отделочные материалы наружных ограждающих конструкций:

- Ограждающие конструкции – сэндвич панель (120 мм).
- Оконное заполнение - стеклопакеты однокамерные.

ж) описание решений по светоограждению объекта, обеспечивающих безопасность полета воздушных судов (при необходимости);

В связи с относительно небольшой высотой объекта и отсутствием вблизи застройки взлетно-посадочных полос воздушных судов, мероприятия по светоограждению, обеспечивающих безопасность полета воздушных судов не предусматривались.

з) описание и обоснование принятых объемно-планировочных решений объекта капитального строительства, обеспечивающих в том числе соблюдение санитарно-эпидемиологических требований;

В проекте приняты следующие объемно-планировочные и инженерные решения объекта, обеспечивающие в том числе соблюдение санитарно-эпидемиологических требований:

- Для защиты железобетонной фундаментной плиты от воздействий внешней среды проектом предусмотрено использование обмазочной гидроизоляции.
- В целях снижения загазованности помещений и удаления избытков тепла от технологического оборудования и солнечной радиации предусматривается система вентиляции и кондиционирования. Вентиляция предусмотрена с механическим побуждением. Архитектурными решениями предусмотрены места для размещения вентиляционных решеток приточной вытяжной вентиляции (2 шт.) и декоративной корзины для размещения внешнего блока кондиционера на дворовом фасаде здания по оси 6. Системы вентиляции и кондиционирования монтируется арендаторами после ввода здания в эксплуатацию в соответствии с корпоративными стандартами и действующими нормативными требованиями.

Специальные конструктивные мероприятия по обеспечению безопасного уровня электромагнитных и иных излучений не требуются. Все применяемые материалы

соответствуют государственным санитарно-эпидемиологическим правилам и нормативам.

з(1) сведения о номенклатуре, компоновке и площадях основных производственных, экспериментальных, сборочных, ремонтных и иных цехов, а также лабораторий, складских и административно-бытовых помещений, иных помещений вспомогательного и обслуживающего назначения - для объектов производственного назначения;

Объект не является объектом производственного назначения.

з(2) обоснование номенклатуры, компоновки и площадей помещений основного, вспомогательного, обслуживающего назначения и технического назначения - для объектов непроизводственного назначения;

Номенклатура, компоновка, площади и прочие характеристики проектируемого зданий приняты на основании задания на проектирование.

Основные технико-экономические показатели объекта:

- Площадь земельного участка – 7 474,6 кв.м.
- Площадь твёрдых покрытий – 2 234,05 кв.м.
- Площадь озеленения – 4 676,3 кв.м. (62,43 % от площади участка).
- Площадь застройки – 573,5 кв.м.
- Общая площадь здания – 553,86 кв.м.
- Количество машино-мест – 13 м/м.
- Строительный объем – 2 852,4 куб.м.
- Количество этажей – 1 этаж.
- Высота здания от земли – 5,2 м.

План на отметке 0.000

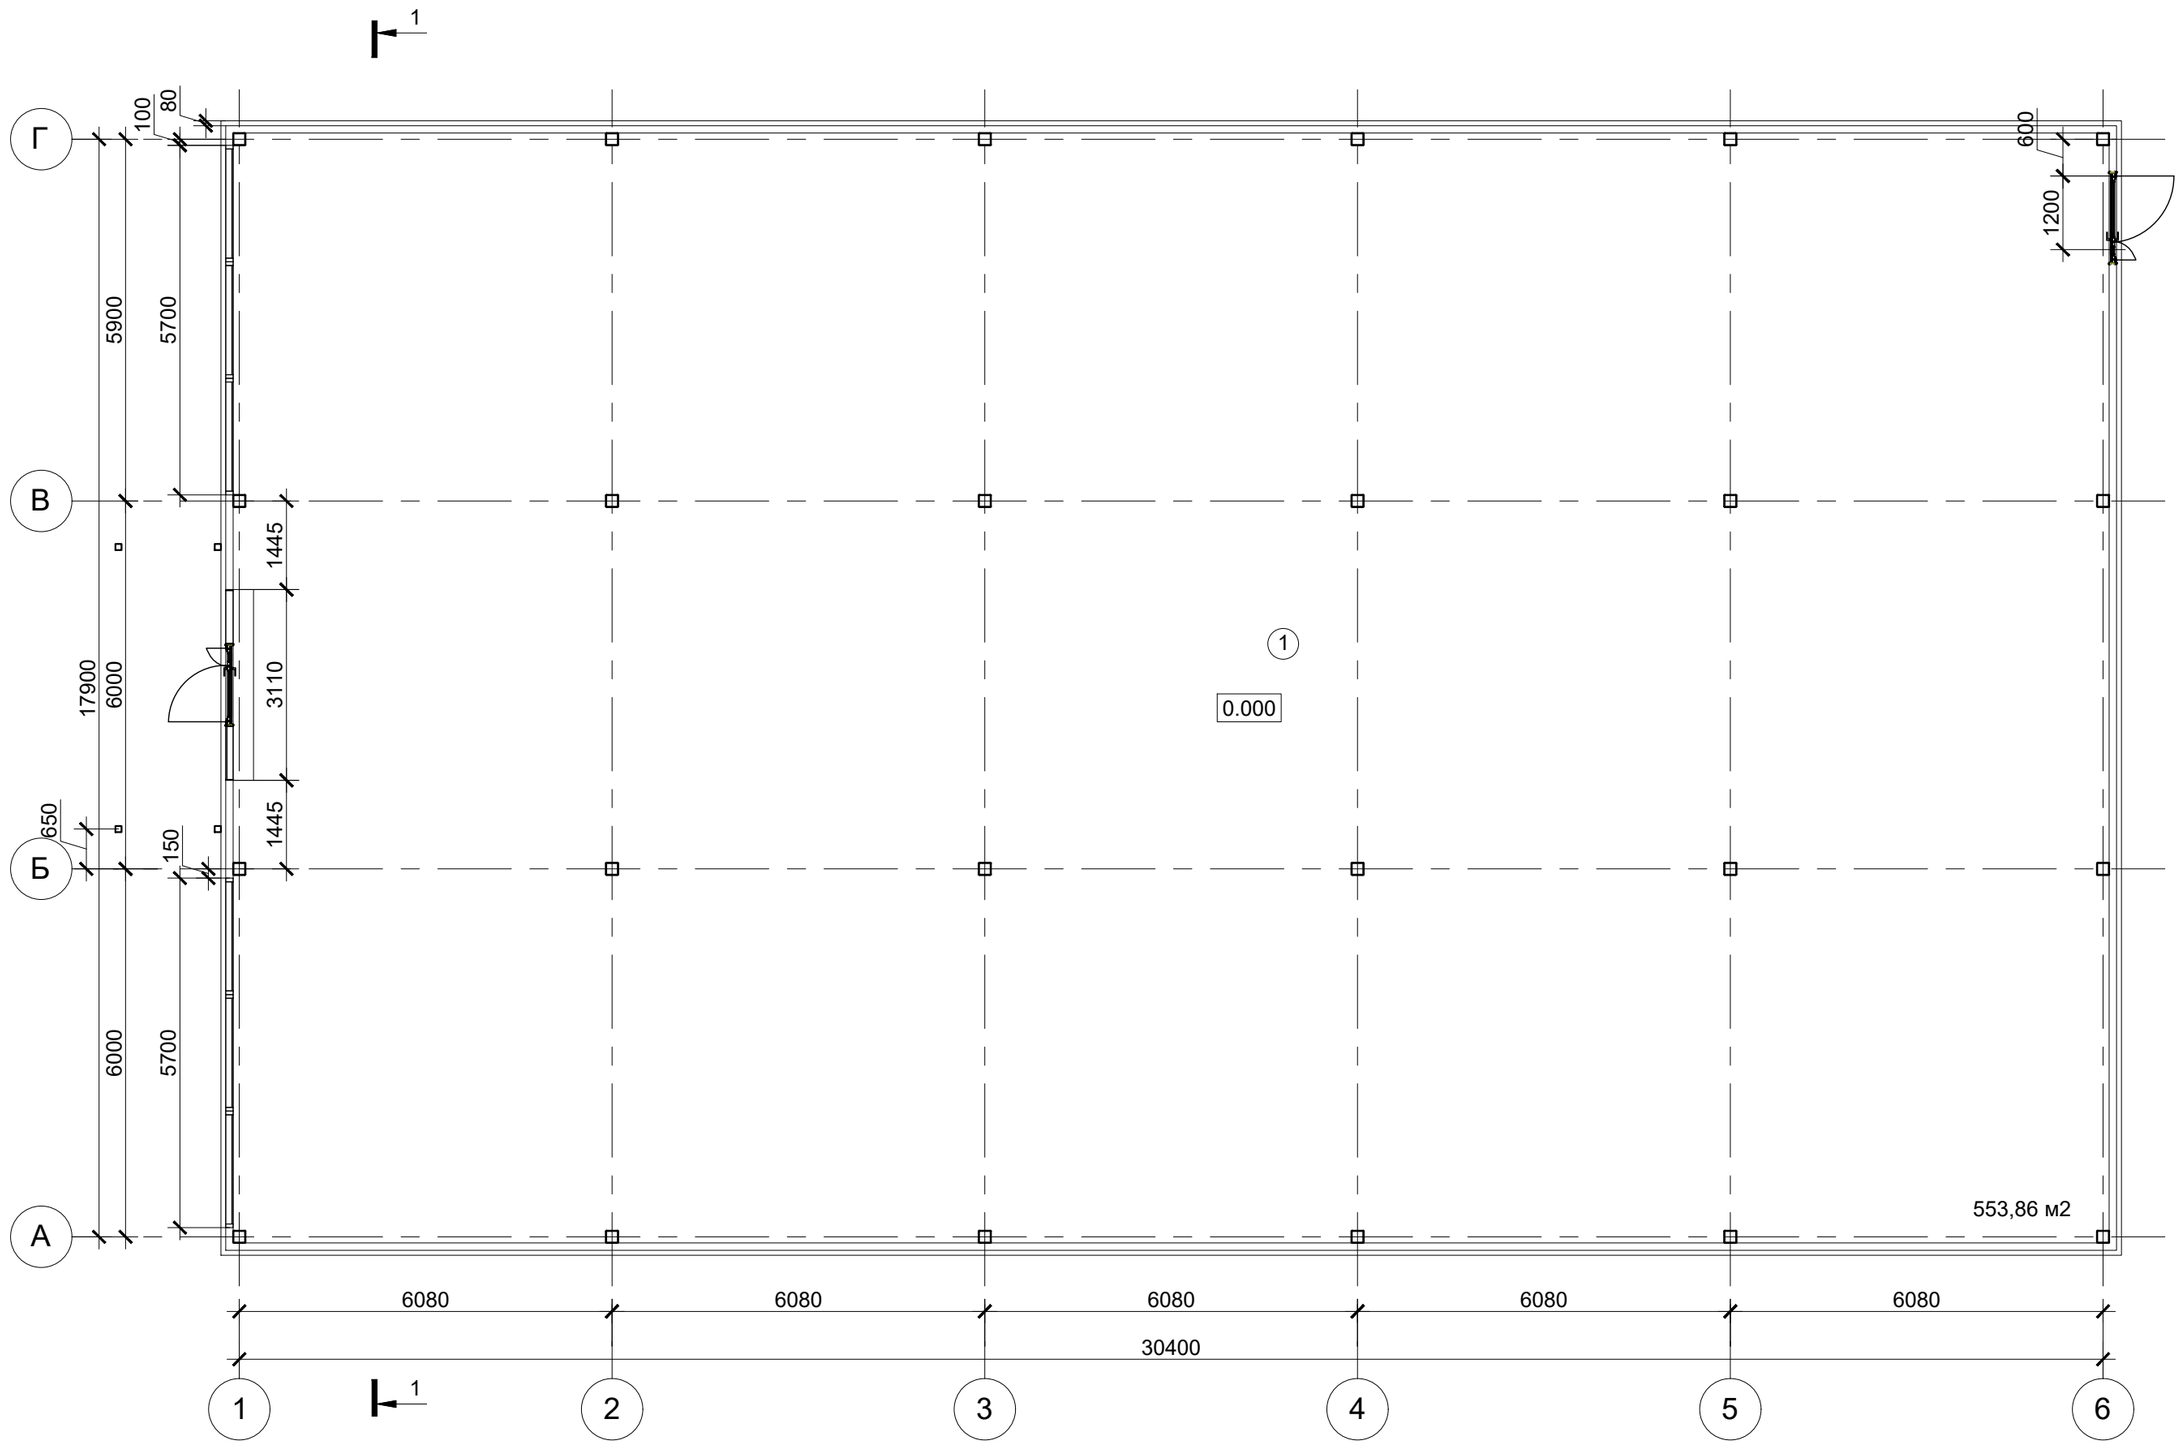

Разрез 1-1

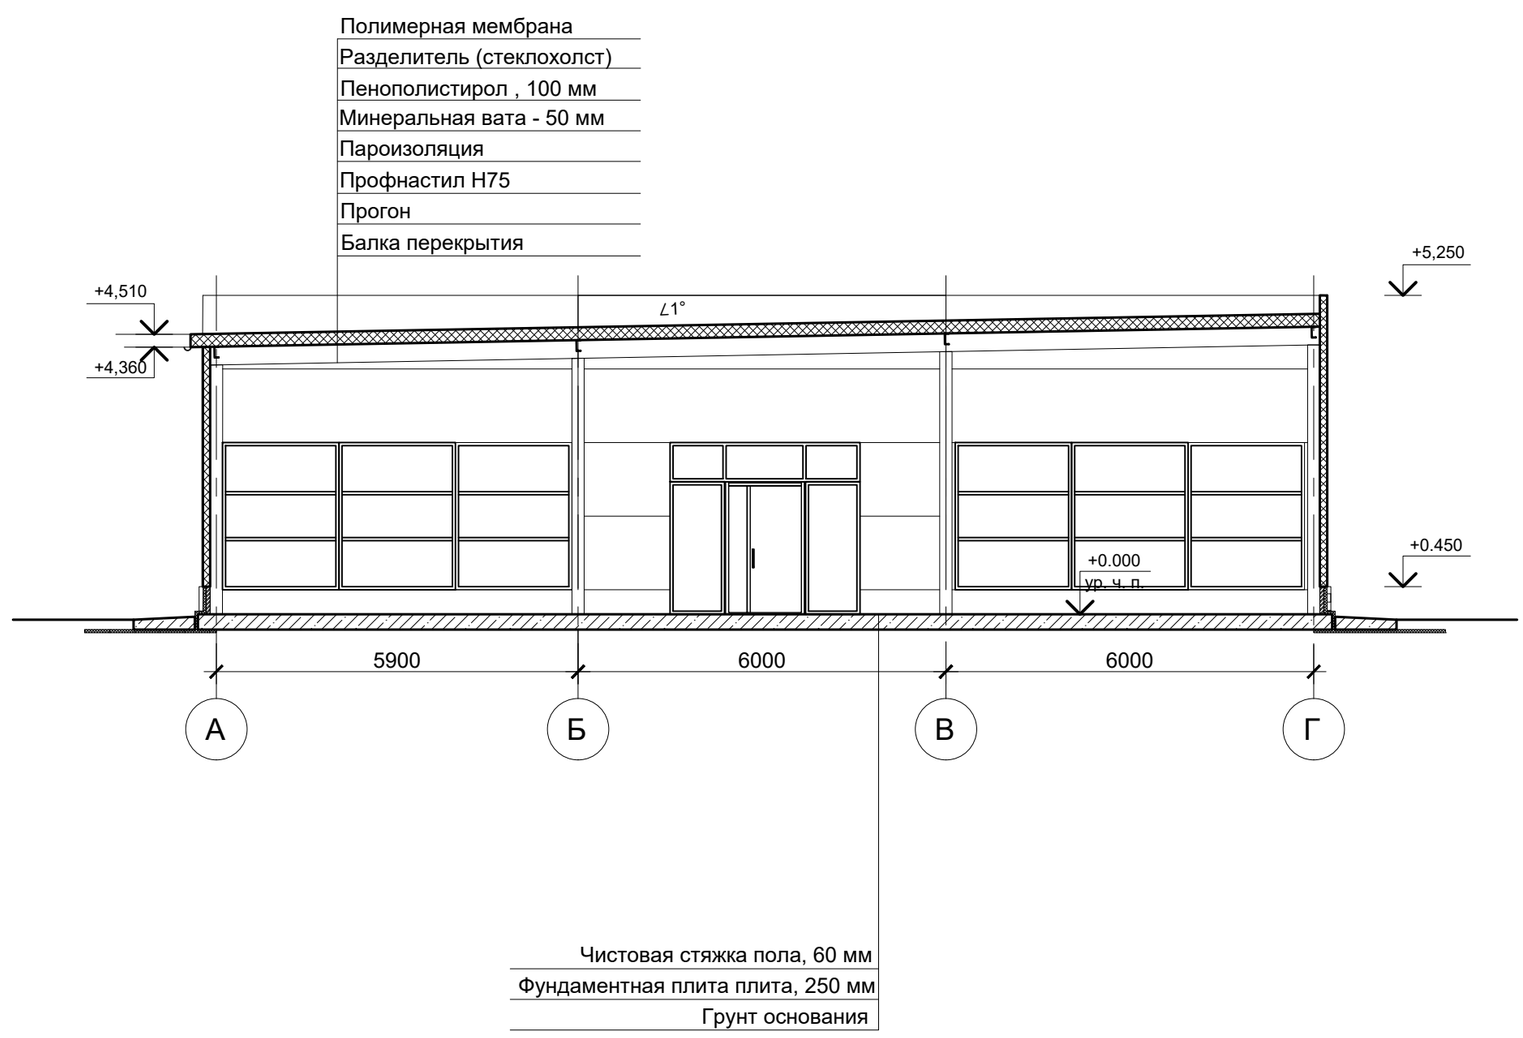

Примечание:

1. Установить снегозадержатели кровельные для ПВХ кровель («Технониколь»);
2. Установить систему водоотвода на край свеса кровли.

Изм.	Кол.уч	Лист	№док.	Подп.	Дата	06-06/24-АР
						"Здание магазина"по адресу: Ленинградская область,Сланцевский муниципальный район, Сланцевское городское поселение, ул. Маяковского, д. 18, Кадастровый номер земельного участка – 47:28:0301052:16
Выполнил		Михайлова			07/24	Здание магазина
Проверил		Гущин			07/24	Стадия: П; Лист: 1; Листов:
Н.контроль		Лебедев			07/24	План 1 этажа на отм 0.000, Разрез 1-1
ГИП		Гущин			07/24	ООО "ПК "КиТ"

Взам. инв. №

Подп. и дата

Инв. № подл.

Формат А2К

Фасад в осях 1-8

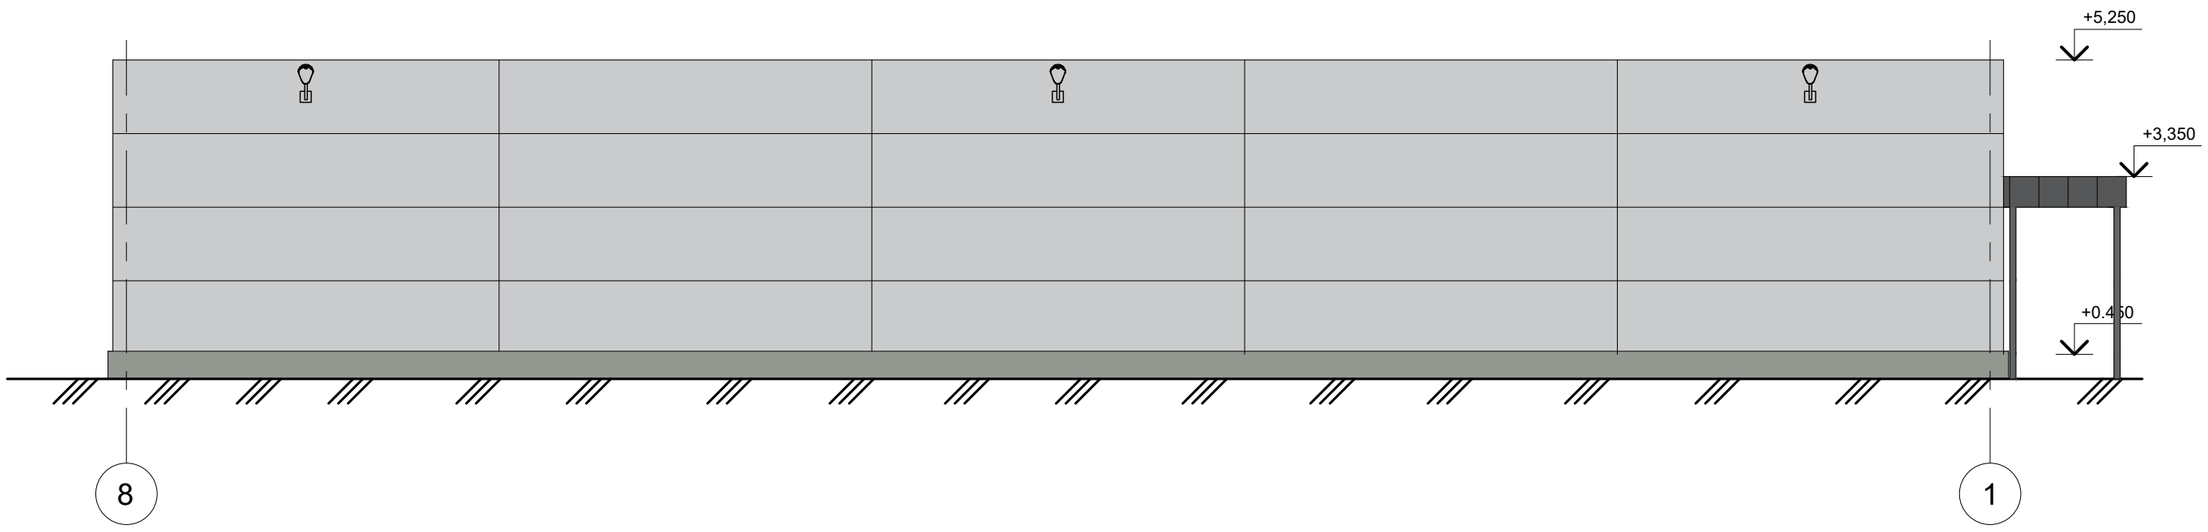

Фасад в осях 1-8

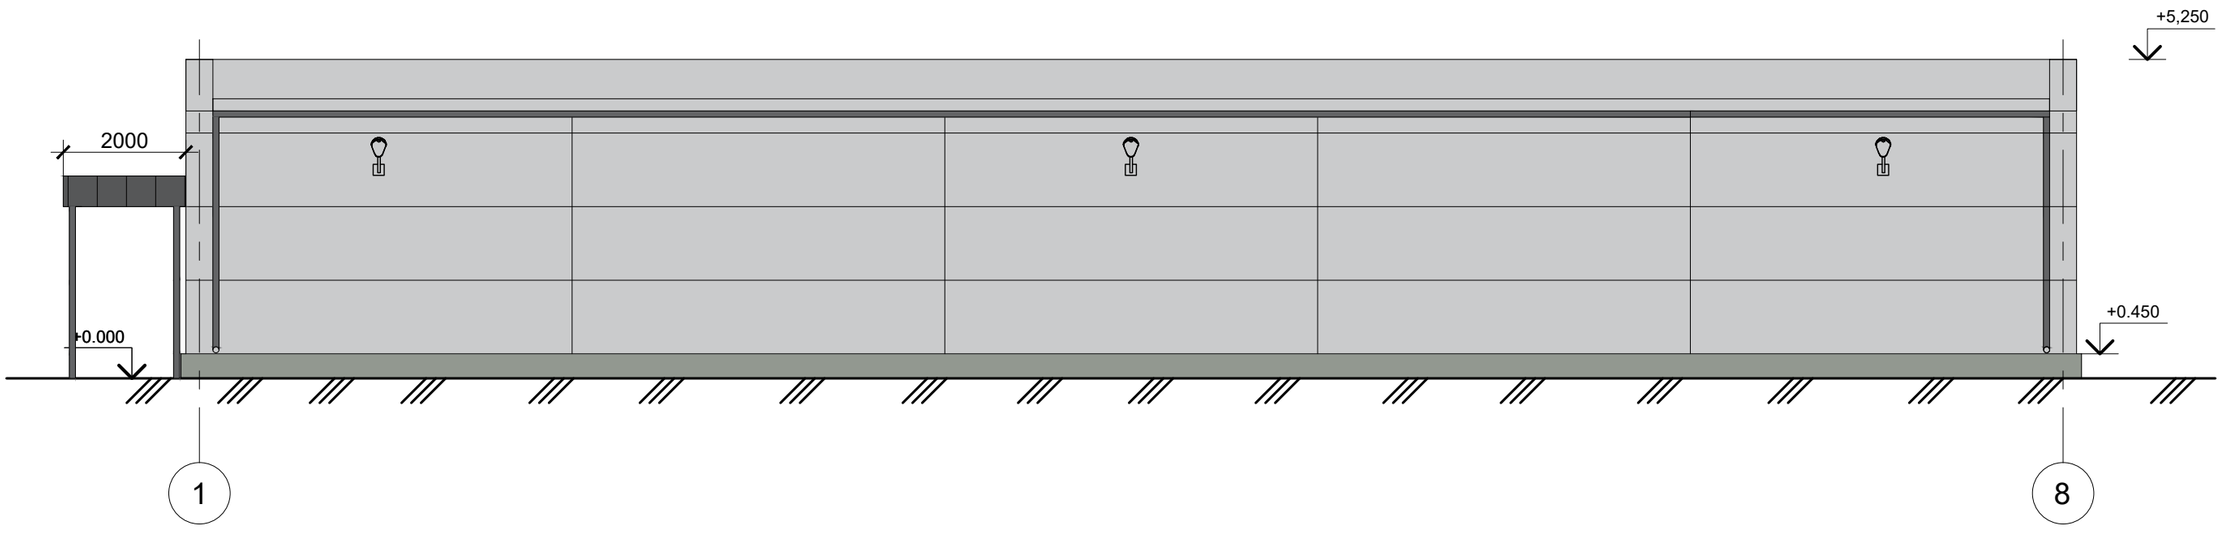

Фасад в осях А-Г

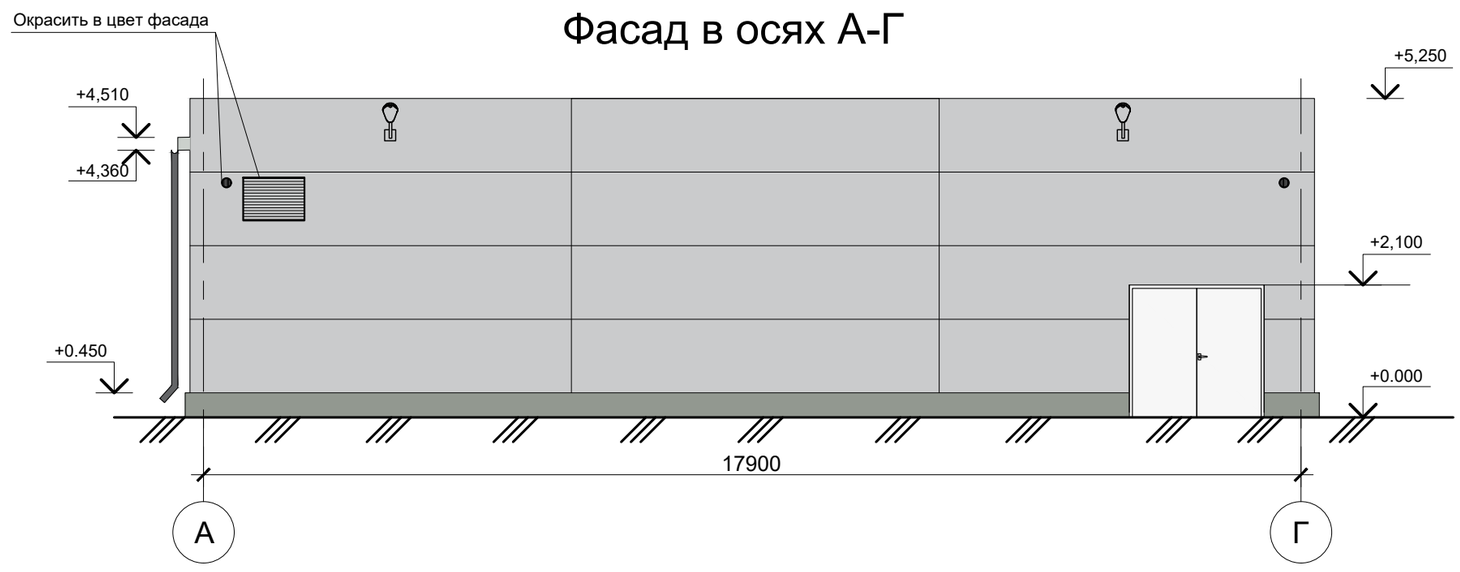

Фасад в осях Г-А

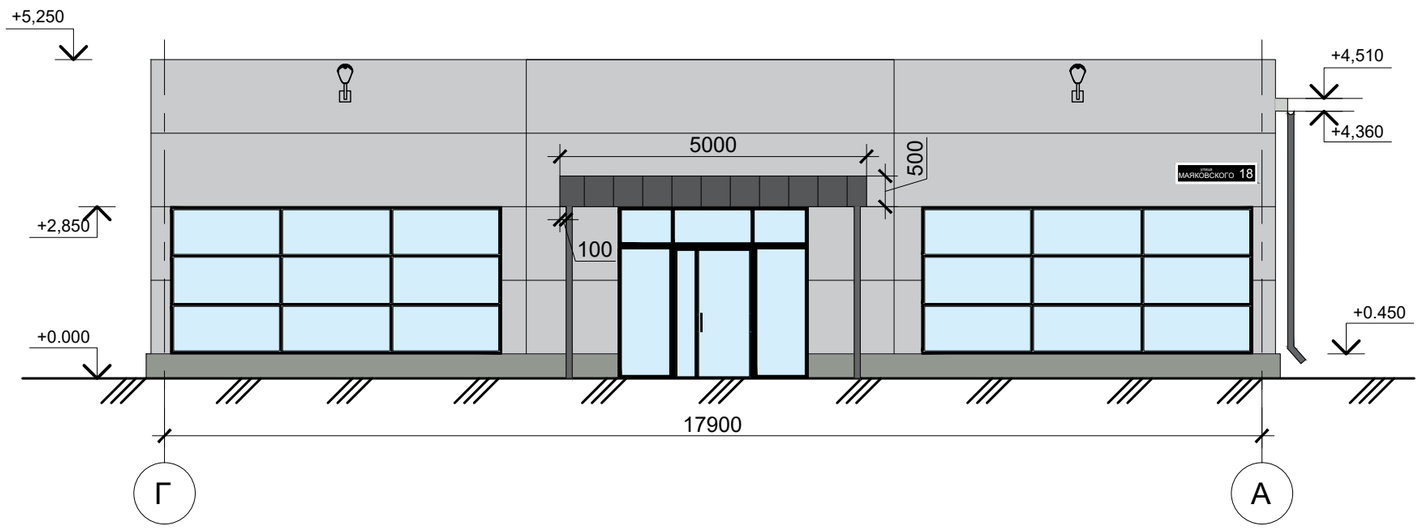

Сэндвич панель
цвет: NCS S 2500-N

Металлическая касетная
панель цвет: NCS S 7500-N

Цоколь из колотого
облицовочного камня СКЦ
цвет: NCS S 3502-G

Оконные и дверные блоки,
водосточная система, стойки
цвет: RAL 8019

Согласовано

Взам. инв. №

Подп. и дата

Инв. № подл.

						06-06/24-АР		
						"Здание магазина"по адресу: Ленинградская область,Сланцевский муниципальный район, Сланцевское городское поселение, ул. Маяковского, д. 18, Кадастровый номер земельного участка - 47:28:0301052:16		
Изм.	Кол.уч.	Лист	№док.	Подп.	Дата			
Выполнил		Михайлова			07/24	Здание магазина	Стадия	Лист	Листов
Проверил		Гущин			07/24		П	2	
Н.контроль		Лебедев			07/24	Фасады 1-8, 8-1, А-Г, Г-А М1:100	ООО "ПК "КиТ"		
ГИП		Гущин			07/24				

Формат А2К