ART-GLOBAL
ДИЗАЙН ВРЕМЕНИ

Индивидуальный предприниматель Николаев Артем Николаевич
Свидетельство СРО-П-140-27022010 от 29 апреля 2022 г.

Заказчик: _____ (подпись) Арджа Д.М (ФИО)

Капитальное строительство складского здания, по адресу Ленинградская область, Всеволожский муниципальный район, Колтушское сельское поселение, кадастровый номер земельного участка 47:07:1047005:6790

ПРОЕКТНАЯ ДОКУМЕНТАЦИЯ

Архитектурные решения

Раздел 3

Шифр: 6790-04/2024-АР

Подрядчик:

И.П. Николаев А. Н.

генеральный директор (должность)	_____	(подпись)	Николаев А.Н. (ФИО)
главный инженер проекта (должность)	_____	(подпись)	Демин А.С. (ФИО)

Санкт-Петербург
2024 г.

Содержание раздела

Обозначение	Наименование	Примечание
6790-04/2024-АР	Содержание тома 1	стр. 1
	Текстовая часть	стр. 3
	Графические материалы	стр. 11

Перечень графических материалов

Обозначение	Наименование	Примечание
Лист 1	Фасады: А-А; Г-Г Фасады: -1; 7-7	
Лист 2	План на отметке 0.000	

Общее количество листов - 13

Согласовано

Взам. инв. №

Подп. и дата

Инв. № подл.

Изм.	Кол.у	Лист	№	Подпись	Дата
Ген. дирек		Николаев А.			04.24
Разработал		Демин А			04.24
Н. контр.		Демин С			04.24

6790-04/2024-АР

Архитектурные решения

Стадия	Лист	Листов
П	1	13

ИП Николаев Артем Николаевич

Оглавление

1 Общие данные..... 3

1.1 Общая информация об объекте..... 3

1.2 Нормативные ссылки 4

2.1 Задание на проектирование..... 4

1.3 Прилагаемые документы 5

1.4 Район строительства..... 5

Географическое положение 5

Климат.. .....

2 Описание и обоснование внешнего и внутреннего вида объекта капитального строительства, его пространственной, планировочной и функциональной организации 7

2.1 Конструктивные и архитектурно-планировочные решения 7

2.2 Перечень основных конструкций 7

3 Обоснование принятых объемно-пространственных и архитектурно-художественных решений, в том числе в части соблюдения предельных параметров разрешенного строительства объекта капитального строительства..... 8

3.1 Обоснование принятых архитектурных решений в части обеспечения соответствия зданий, строений и сооружений установленным требованиям энергетической эффективности..... 8

3.2 Перечень мероприятий по обеспечению соблюдения установленных требований энергетической эффективности к архитектурным решениям, влияющим на энергетическую эффективность зданий, строений и сооружений..... 8

4 Описание и обоснование использованных композиционных приемов при оформлении фасадов и интерьеров объекта капитального строительства..... 9

5 Описание решений по отделке помещений основного, вспомогательного, обслуживающего и технического назначения..... 9

6 Описание архитектурных решений, обеспечивающих естественное освещение помещений с постоянным пребыванием людей..... 9

7 Описание архитектурно-строительных мероприятий, обеспечивающих защиту помещений от шума, вибрации и другого воздействия..... 10

8 Описание решений по декоративно-художественной и цветовой отделке интерьера - для объекта непроизводственного назначения 10

Графические материалы..... 11

1. Общие данные

1.1 Общая информация об объекте

Название объекта: Капитальное строительство складского здания, по адресу Ленинградская область, Всеволожский муниципальный район, Колтушское сельское поселение, кадастровый номер земельного участка 47:07:1047005:6790.

Назначение объекта: склад для хранения негорючих промышленных и хозяйственных товаров.

Площадь застройки составляет 1314.8 $м^2$.

Общая площадь здания составляет 1296.0 $м^2$.

Габариты здания:

длина- 54.24 м;

ширина-24.24 м.;

высота по коньку кровли -8.830 м.

Принадлежность к объектам транспортной инфраструктуры и к другим объектам, функционально технологические особенности которых влияют на их безопасность: не имеет.

Возможность возникновения опасных природных процессов, явлений и техногенных воздействий на территории, на которой будет осуществляться строительство объекта: нет.

Степень огнестойкости здания – II.

Класс функциональной пожарной опасности – Ф 5.2 (№123-Ф-3 ст.32 п.5)

Наличие помещений с постоянным пребыванием людей: Нет.

Уровень ответственности согласно пункту 7 части 1 и части 7 статьи 4 Федерального закона от 30 декабря 2009 г. N 384-ФЗ "Технический регламент о безопасности зданий и сооружений": нормальный.

Вид деятельности объекта: складское хранение, обработки товаров и грузов на складе, упаковка, маркировка и переупаковка негорючих промышленных и хозяйственных товаров.

Режим работы объекта: Круглогодичный - 365 дней в году 8 часа в сутки.

Вид строительства: Новое строительство.

1.2 Нормативные ссылки

Раздел «Архитектурные решения» проекта по объекту Капитальное строительство одноэтажного складского здания, по адресу Ленинградская область, Всеволожский муниципальный район, Колтушское сельское поселение, кадастровый номер земельного участка 47:07:1047005:6790 выполнен в соответствии со следующими нормативными документами:

— Градостроительный кодекс Российской Федерации от 29 декабря 2004 г. № 190-ФЗ.

— Постановление Правительства Российской Федерации от 16 февраля 2008 года № 87 «О составе разделов проектной документации и требования к их содержанию».

— Федеральный закон Российской Федерации от 30 декабря 2009 г. № 384-ФЗ «Технический регламент о безопасности зданий и сооружений».

— Федеральный закон Российской Федерации от 22 июля 2008 г. № 123-ФЗ «Технический регламент о требованиях пожарной безопасности».

— Федеральный закон Российской Федерации от 23 ноября 2009 г. № 261-ФЗ «Об энергосбережении и о повышении энергетической эффективности, и о Внесении изменений В отдельные законодательные акты Российской Федерации».

— СП 131.13330.2018 (СНиП 23-01-99). Строительная климатология.

— СП 1.13130.2020 Системы противопожарной защиты. Эвакуационные пути и выходы.

— СП 52.13330.2016. Естественное и искусственное освещение. Актуализированная редакция СНиП 23-05-95.

— СП 51.13330.2011. Защита от шума. Актуализированная редакция СНиП 23-03-2003.

— СП 48.13330.2019. Организация строительства.

— ГОСТ 12.1.004-91. ССБТ. Пожарная безопасность. Общие требования.

— ГОСТ 12.1.003-2014. ССБТ. Шум. Общие требования безопасности.

Принятые в проекте технические и проектные решения и материалы соответствуют требованиям Государственных Технических Регламентов, Строительных Норм и Правил, Государственных стандартов, Правил пожарной безопасности, санитарно-гигиенических правил и норм, экологических, природоохранных и других норм, инструкций, стандартов и требований, действующих на территории Российской Федерации на дату

выпуска, и обеспечивают безопасную для жизни и здоровья людей эксплуатацию объекта при соблюдении предусмотренных проектом решений.

1.3 Прилагаемые документы

Раздел «Архитектурные решения» проекта по объекту Капитальное строительство одноэтажного складского здания, по адресу Ленинградская область, Всеволожский муниципальный район, Колтушское сельское поселение, кадастровый номер земельного участка 47:07:1047005:6790 выполнен на основании следующих документов:

— Задание на проектирование;
— Отчетная документация по результатам инженерных изысканий;
— Утвержденный и зарегистрированный в установленном порядке градостроительный план земельного участка, предоставленного для размещения объекта капитального строительства;
— Технические условия на подключение к энергоресурсам

Решения о согласовании размещения объекта.

1.4 Район строительства

Географическое положение.

Проектируемое здание, площадь застройки составляет 1314.8 м^2, расположено на территории участка площадью 2500 кв. м. Кадастровый номер земельного участка 47:07:1047005:6790, по адресу Ленинградская область, Всеволожский район, Колтушское сельское поселение, примерно в двух километров от деревни Мяглово по направлению Мяглово – поселок Свердлова.

Климат.

Климат исследуемой территории характеризуется как умеренно-континентальный с влиянием морского. Сильная циклоническая деятельность обуславливает многолетнюю изменчивость погоды и её неустойчивость в течение года. Зима умеренно холодная с частыми оттепелями, снежный покров неустойчив.

В соответствии со схемой климатического районирования для строительства (СП 131.13330.2018 «Строительная климатология. Актуализированная редакция СНиП 23-01-99») территория будущего строительства находится в климатической зоне II В.

Средняя температура января -8...-11°С, июля +16...+18°С. Абсолютный максимум температуры +32 °С, абсолютный минимум -32°С.

Наиболее холодными являются восточные районы, наиболее теплыми - юго-западные.

Самый холодный месяц в области - январь или февраль. Средняя температура января на востоке области -10°С, на западе -6°С. Самый теплый месяц во Всеволожском районе - июль. Средняя температура воздуха в этом месяце равна 16,5-17,5°С. Абсолютный максимум температуры воздуха равен +32°С.

Продолжительность периода со средней суточной температурой воздуха выше 5°С на востоке области примерно 160, а на юго-западе - 170 дней. Сумма среднесуточных температур в дни с температурами выше 10°С составляет 1600-1800.

Зимний сезон длится около 6 месяцев с конца октября до начала апреля и характеризуется морозной погодой с высоким снежным покровом и редкими оттепелями. Устойчивые морозы сохраняются до 4 месяцев.

Летний сезон длится 3,5 месяца с конца мая до первой половины октября. Для него типична неустойчивая погода с переменной облачностью и проходящими осадками.

Переходные сезоны имеют затяжной характер, весной часты возвратные холода, осенью же, на фоне пасмурной дождливой погоды, ясные дни бывают относительно редко.

Для области характерна высокая облачность. Наименьшая облачность - весной и в начале лета, наибольшая - осенью.

Вся территория Ленинградской области находится в зоне избыточного увлажнения. Количество осадков за год 600-700 мм. Наибольшее количество осадков выпадает на возвышенностях, максимум - на Лемболовской. Минимальное количество осадков выпадает на прибрежных низменностях. Самое большое количество осадков выпадает летом и осенью. В зимний период осадки выпадают в основном в виде снега. Постоянный снежный покров появляется во второй половине ноября - первой половине декабря. Сходит снег во второй половине апреля.

На территории района преобладают ветры юго-западных и западных направлений, несущие влажный воздух атлантического происхождения. Скорость ветра в зимние месяцы составляет 3,5-4,0 м/с, на побережье Ладожского озера она увеличивается до 5,5-6,0 м/с. В теплое время года ветры ослабевают. Сильные ветры (15 м/с и выше) отмечаются преимущественно в холодный период.

В соответствии с СП 20.13330.2016 приложения Е карт районирования территории Российской Федерации по климатическим характеристикам участок работ относится по весу снегового покрова к III району; по давлению ветра – к I району.

Нормативная снеговая нагрузка для III снегового района - 150 кг/м^2 (1,5 кПа).
Расчетная снеговая нагрузка для III снегового района - 210 кг/м^2 (2,1 кПа).
Нормативная ветровая нагрузка для I ветрового района - 32 кг/м^2.

2. Описание и обоснование внешнего и внутреннего вида объекта капитального строительства, его пространственной, планировочной и функциональной организации

2.1 Конструктивные и архитектурно-планировочные решения:

Данный объект капитального строительства является одноэтажным прямоугольным в плане зданием. Габариты здания в плане – 24.240 м на 54.240 м.

2.2 Перечень основных конструкций

Фундамент — железобетонный стаканного типа ФМ-8-1; ФМ-2 серии 3.016.2-13. Каркас здания спроектирован из:

— колонны: двутавр №30К1, класс металла С255 ГОСТ 27772-88*

— фермы треугольные, двухскатные из металлических профильных труб,

— кровля из кровельных сэндвич-панелей толщиной 150 мм по металлическим прогонам.

Стены наружные – самонесущие, конструкция стен, согласно теплотехническому расчету, выполнены из стеновых сэндвич-панелей толщиной 120 мм.

Окна - прозрачное заполнение, двухкамерный стеклопакет, глухое заполнение.

Отмостка бетонная 550 мм.

3. Обоснование принятых объемно-пространственных и архитектурно-художественных решений, в том числе в части соблюдения предельных параметров разрешенного строительства объекта капитального строительства

В административном отношении здание находиться в границах промышленной зоны.

Проект предусматривает новое строительство здания.

Планировка участка строящегося здания решена с учетом градостроительной ситуации, в соответствии с требованиями действующих норм и правил.

3.1 Обоснование принятых архитектурных решений в части обеспечения соответствия зданий, строений и сооружений установленным требованиям энергетической эффективности

Проектной документацией предусмотрены оптимальные архитектурные решения, влияющие на энергетическую эффективность здания, и позволяющие исключить нерациональный расход энергетических ресурсов, как в процессе строительства, так и в процессе их эксплуатации проектируемого здания.

3.2 Перечень мероприятий по обеспечению соблюдения установленных требований энергетической эффективности к архитектурным решениям, влияющим на энергетическую эффективность зданий, строений и сооружений

В здании применены следующие энергосберегающие мероприятия:

—В качестве утеплителя ограждающих конструкций здания используются эффективные теплоизоляционные материалы.

—Устанавливаются оконные блоки с двойным остеклением и с высоким сопротивлением теплопередаче.

—Устанавливаются узлы учета энергетических ресурсов.

4. Описание и обоснование использованных композиционных приемов при оформлении фасадов и интерьеров объекта капитального строительства

Формирование архитектурно-планировочной структуры базируется на функциональном пространственном зонировании, которое предполагает пространственный характер организации основных функциональных зон. Для наружной отделки применены современные отделочные материалы в составе современных теплоизоляционных фасадных систем.

5. Описание решений по отделке помещений основного, вспомогательного, обслуживающего и технического назначения

Определяются заказчиком.

6. Описание архитектурных решений, обеспечивающих естественное освещение помещений с постоянным пребыванием людей

Естественное освещение всех помещений - боковое. Во всех помещениях выполняется требование по естественной освещенности в соответствии с ЕП 52.13330.2016 «Естественное и искусственное освещение. Актуализированная редакция СНиП 23-05-95».

Площадь световых проемов составляет не менее 15% от площади помещений.

Светопрозрачные конструкции и осветительная арматура в помещениях предусмотрены на отметках, обеспечивающих доступ для очистки без использования дополнительных механизмов.

7. Описание архитектурно-строительных мероприятий, обеспечивающих защиту помещений от шума, вибрации и другого воздействия

Требуемая по СП 51.13330.2011 «Защита от шума» звукоизоляция обеспечивается следующими мероприятиями:

—Звукоизоляционной защитой наружных ограждающих конструкций.

—Применением конструкций стен с нормируемой звукоизоляцией.

—Для остекления предусмотрены окна с переплетами из ПВХ профиля, с заполнением двухкамерным стеклопакетом, в необходимых случаях снабженные шумозащитными приточными клапанами.

Наружные ограждающие конструкции имеют слоистую структуру — сэндвич-панели.

Для снижения внешнего шума предусмотрено применение оконных блоков со стеклопакетом в переплетах из ПВХ профиля. Монтаж оконных блоков производится с использованием тепло- и звукоизоляционных пенных полиуретановых уплотнителей. В полотнах наружных дверей имеется заполнение из тепло- и звукоизоляционного материала. Для повышения звукоизоляции устанавливается не менее двух контуров уплотняющих прокладок.

Внутренние стены и перегородки запроектированы с нормируемой звукоизоляцией.

8. Описание решений по декоративно-художественной и цветовой отделке интерьера - для объекта непроизводственного назначения

Не требуется.

Часть 2 Графические материалы

Раскладка стеновых сэндвич-панелей по оси Д-Д; А-А

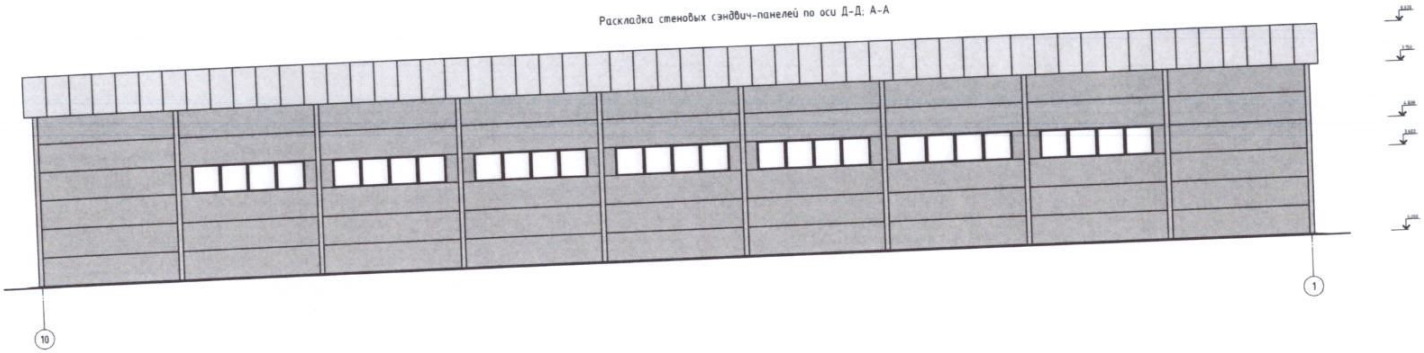

Раскладка стеновых сэндвич-панелей по оси 1

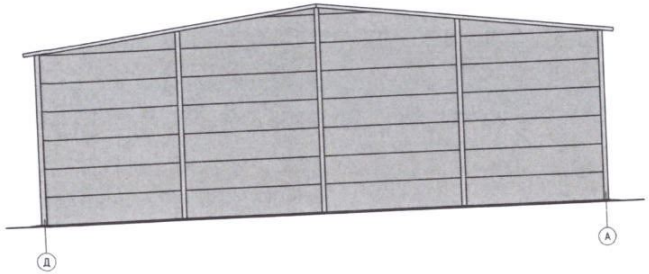

Раскладка стеновых сэндвич-панелей по оси 10

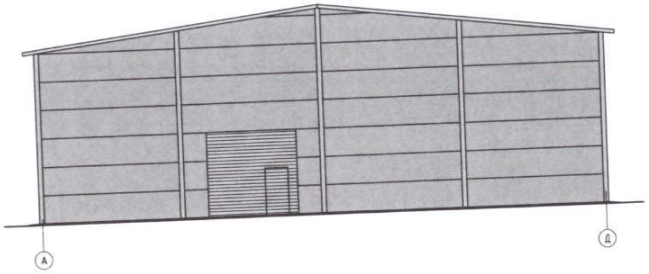

						6796-04/2024-АР			
						Ленинградская область, Выборгский муниципальный округ, Гончаровское сельское поселение, территория, номер 47:03:0126:955			
Изм.	Кол.уч.	Лист	№ док.	Подп.	Дата				
Гл. инженер		Николаев А.				Обезлаженное складское здание	Стадия	Лист	Листов
Разработал		Белов С.					П	1	1
Проверил		Белов А.				Фасады	«Индивидуальный предприниматель Николаев Артем Николаевич»		
							Формат А3х7		

План на отметке 0.000

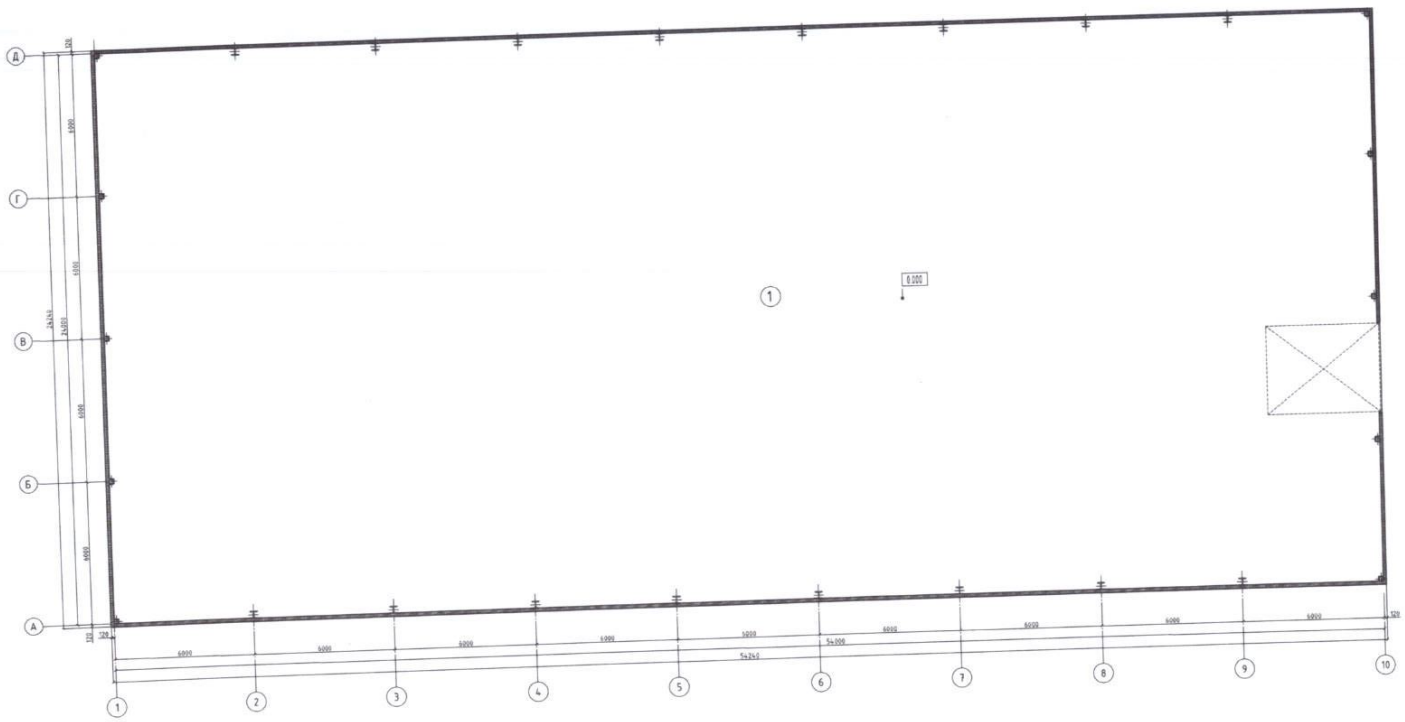

ЭКСПЛИКАЦИЯ ПОМЕЩЕНИЙ

№ на плане	Наименование	Площадь, м²	в комн.	Площадь, в расч. м²	Примечания
1	Помещение	1296.0	1	1296.0	
	ВСЕГО:			1296.0	

						6796.04/2024-АР
Изм.	Кол.уч.	Лист	N док.	Подпись	Дата	Ленинградская область, Всеволожский муниципальный район, Колтушское сельское поселение, кадастровый номер 47:07:1013035:1[illegible]
Гл. инженер		Наговский А			24.24	Одноэтажное складское здание
Разработал		Данчук Е			24.24	План
Проверил		Данчук А				

Стадия	Лист	Листов
Р	2	2

Индивидуальный предприниматель Николаев Артем Николаевич

Формат А4